

건축공간론 스터디

르 코르뷔지에와 페터 Zumthor의 대표적인 건축물을 분석하며,
기둥의 배치나 시야각의 설계 등이 어떻게 동선을 유도하는지 탐구하였습니다.

01 빌라 사보아 Villa Savoye - 르 코르뷔지에 (3p)

02 빌라 라 로셰 Billa La Roche - 르 코르뷔지에 (2p)



03 발스 온천 Vals Therme - 페터 Zumthor (2p)

* 홍익대학교 건축학과 장용순 교수님의 24-2학기 '건축공간론' 수업 내용을 바탕으로 하였으며,
첨부한 그림들은 수업자료를 바탕으로 직접 그렸습니다.

작성자 : 박민지
parmji2111@gmail.com


빌라 사보아

1. 촘촘한 공간 분할

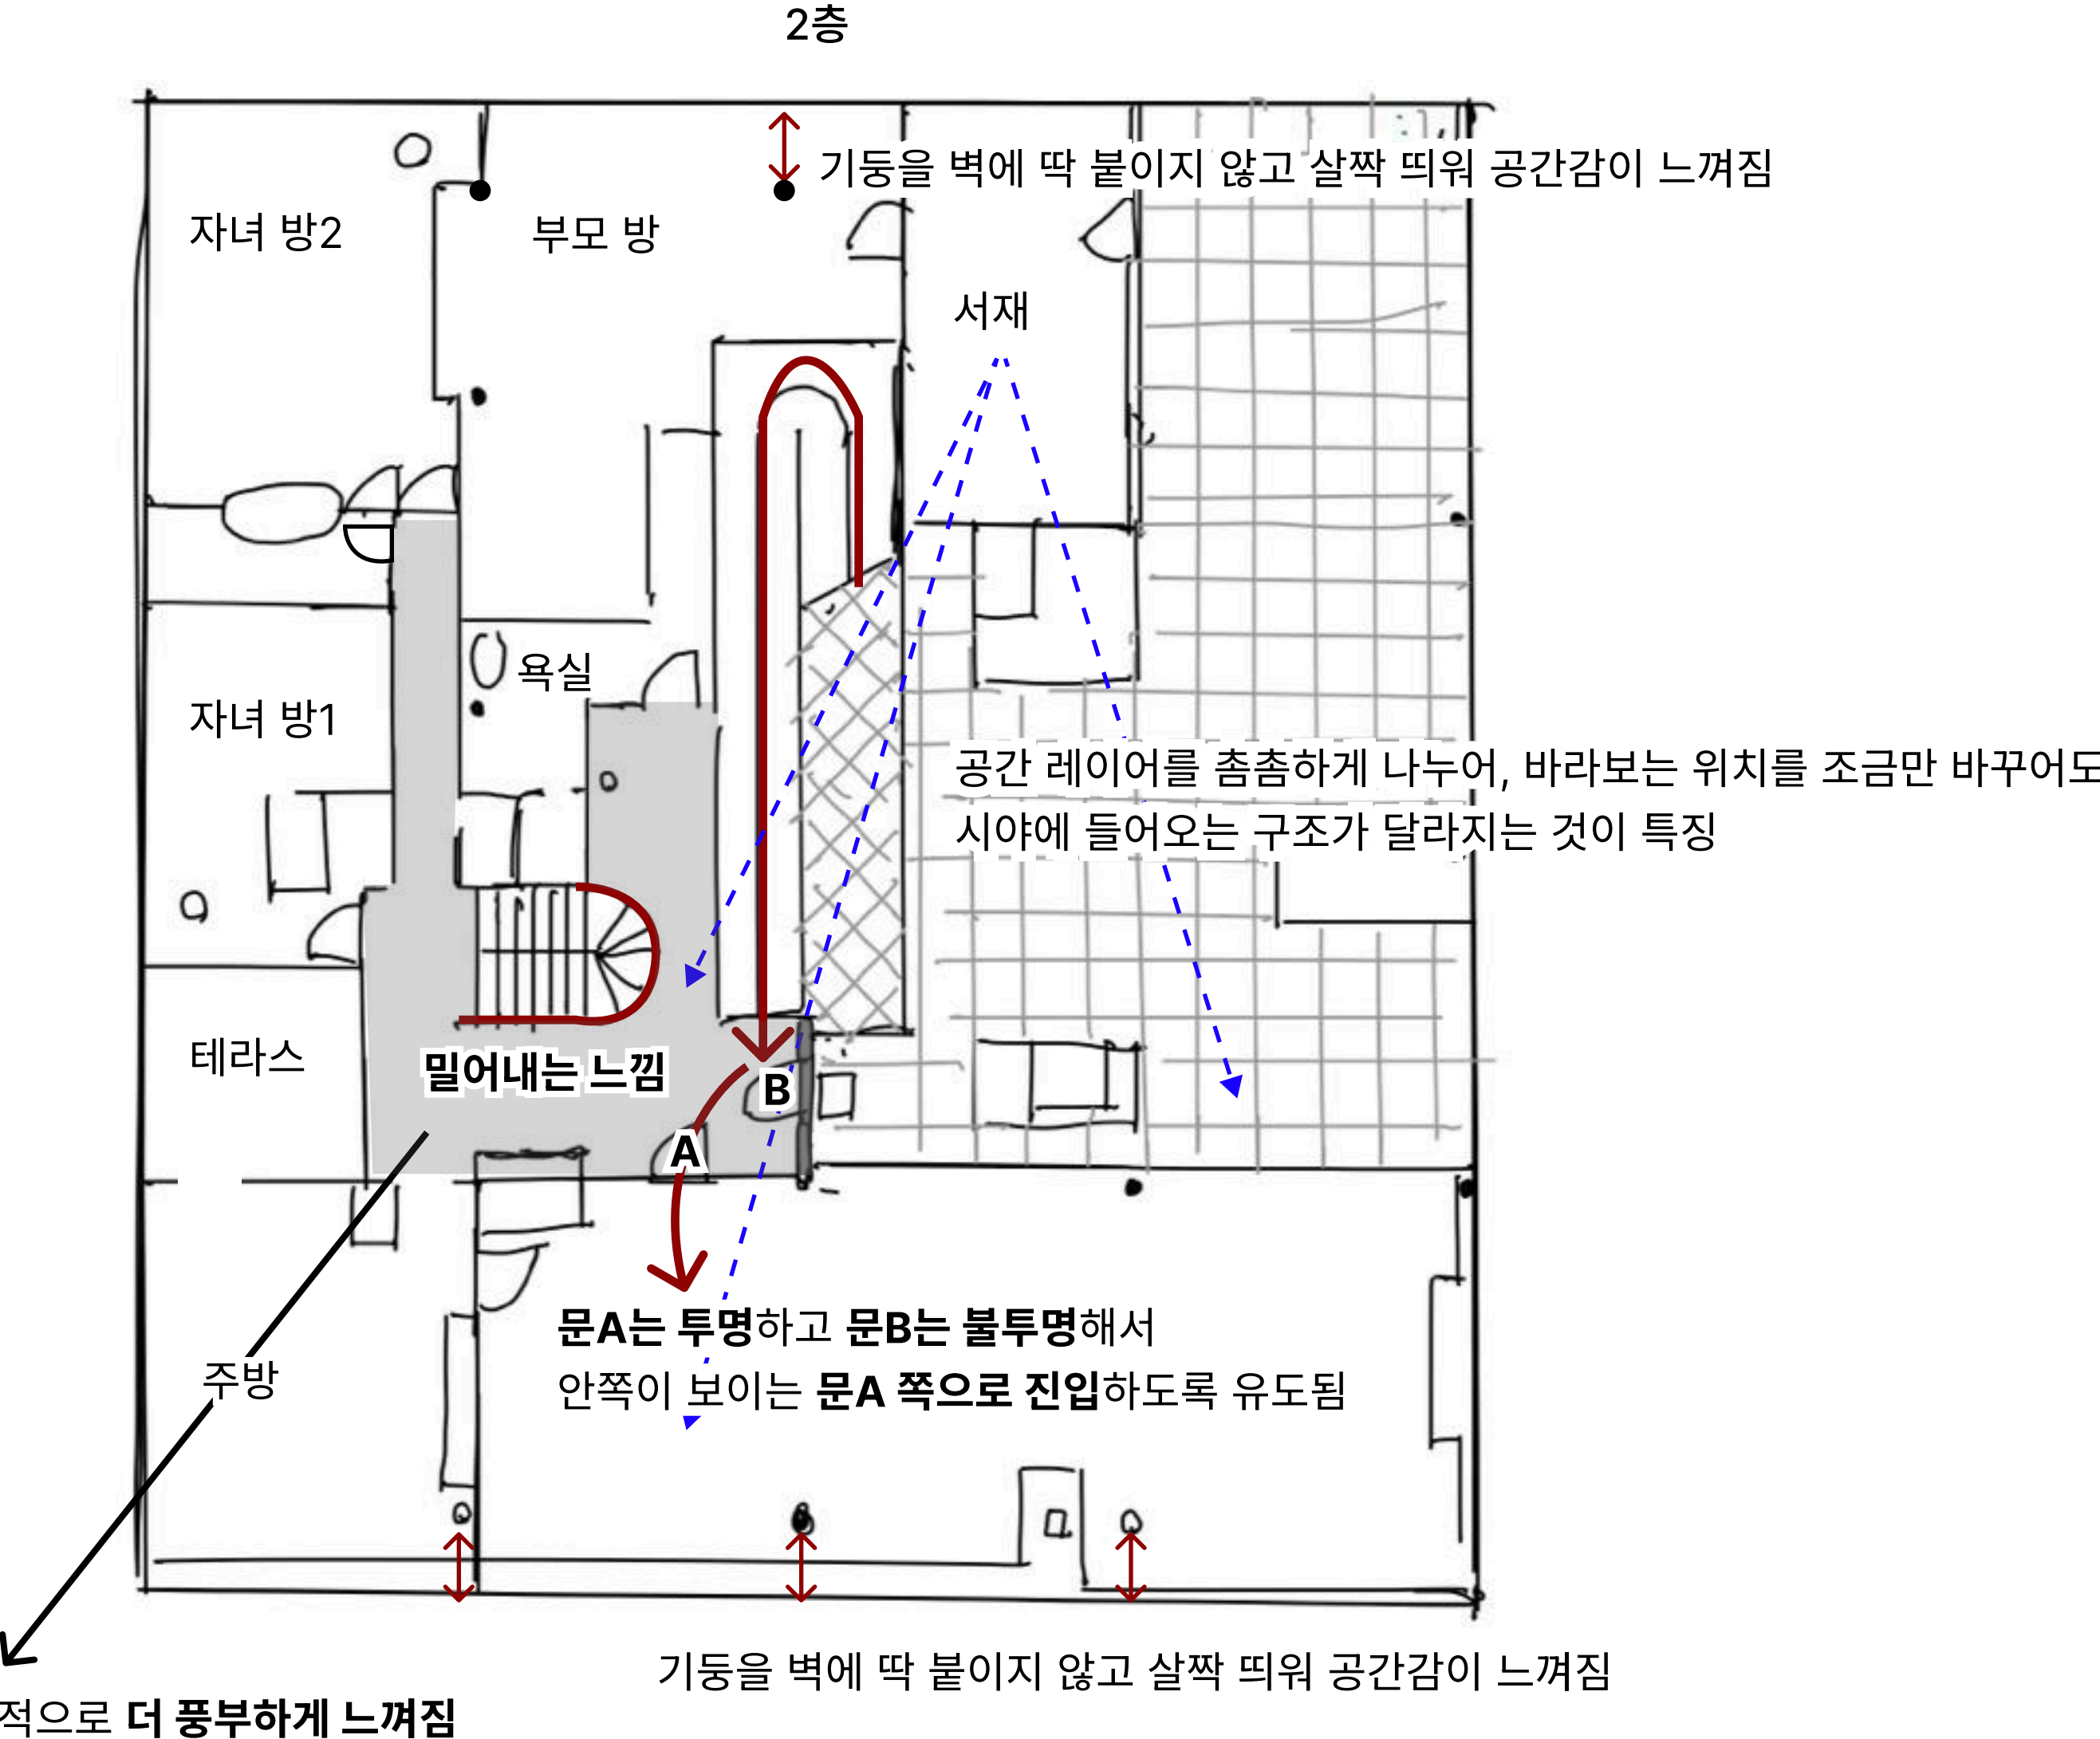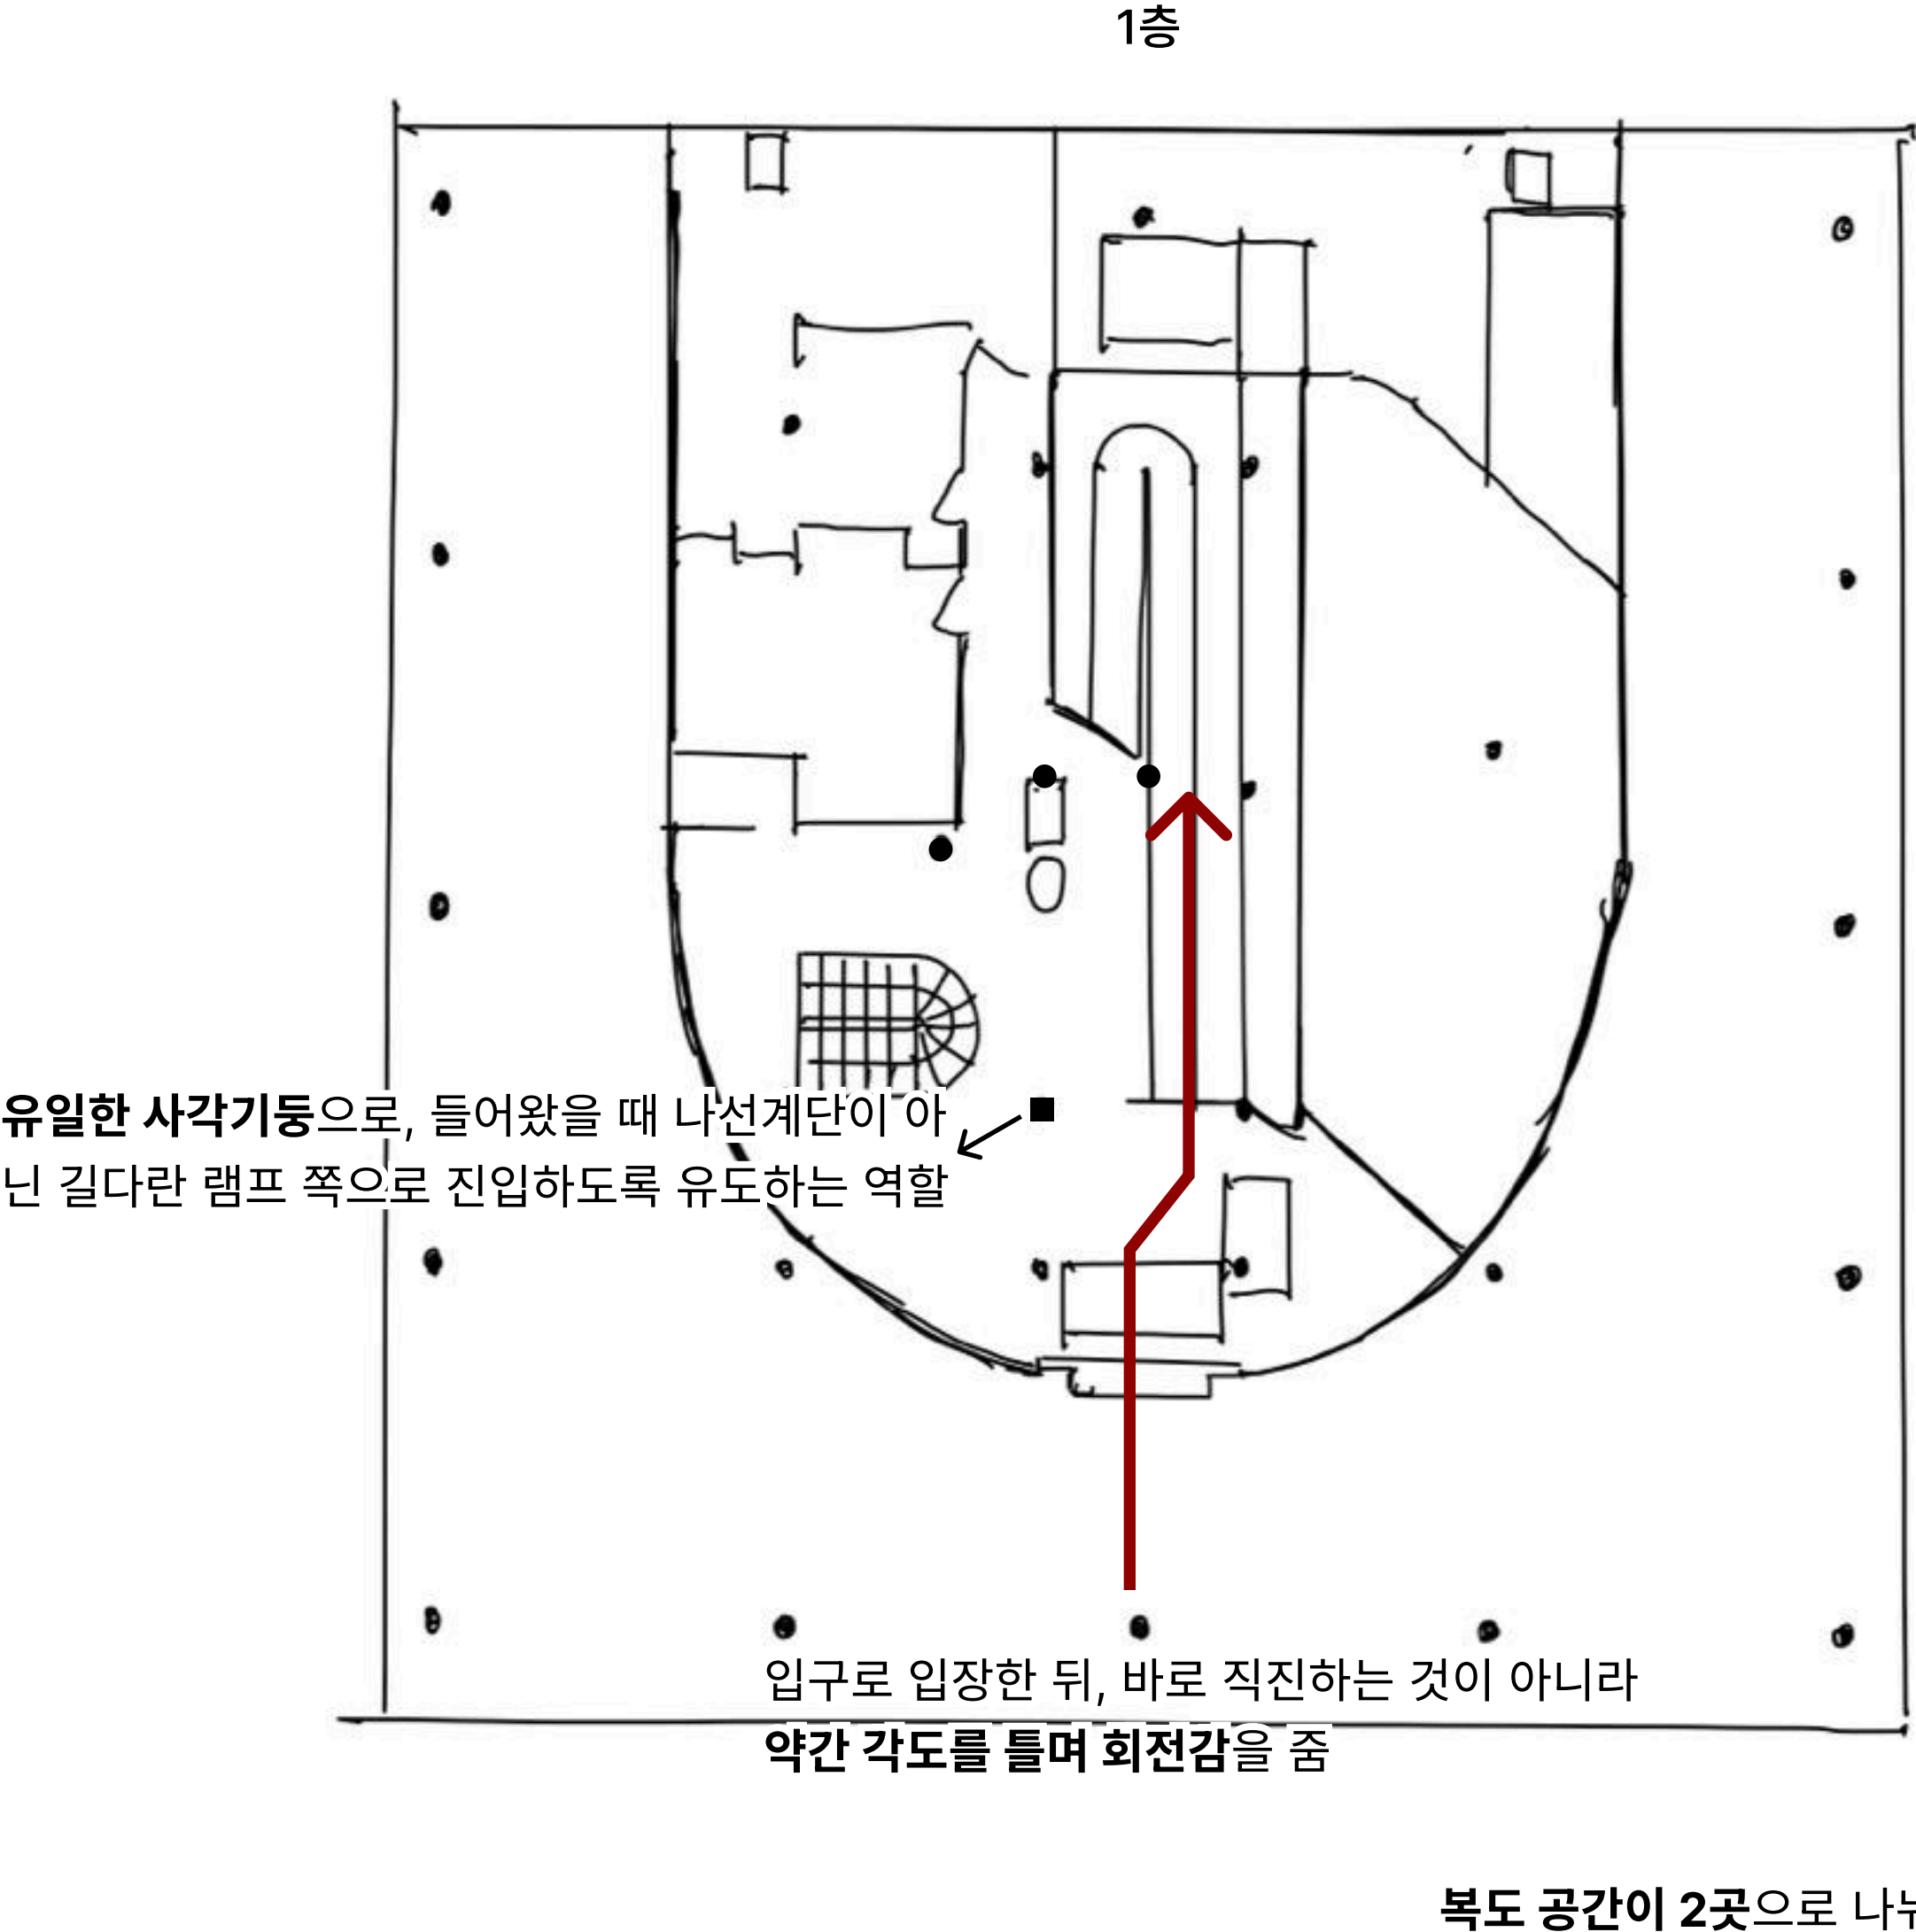

빌라 사보아

2. 진입 루트 설계

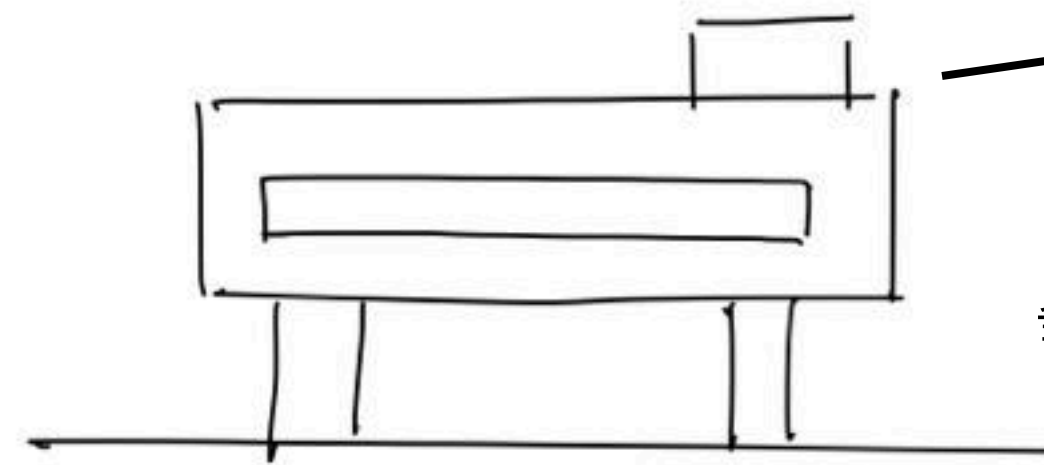


오른쪽에 볼륨 有 → 오른쪽으로 이동하도록 사람들이 유도됨

숲에서 건물 뒤쪽으로 진입


- 창문은 밖에서 볼 땐 뚫린 것 같은 느낌을 줌. 어두운 창틀

빌라 사보아 진입루트

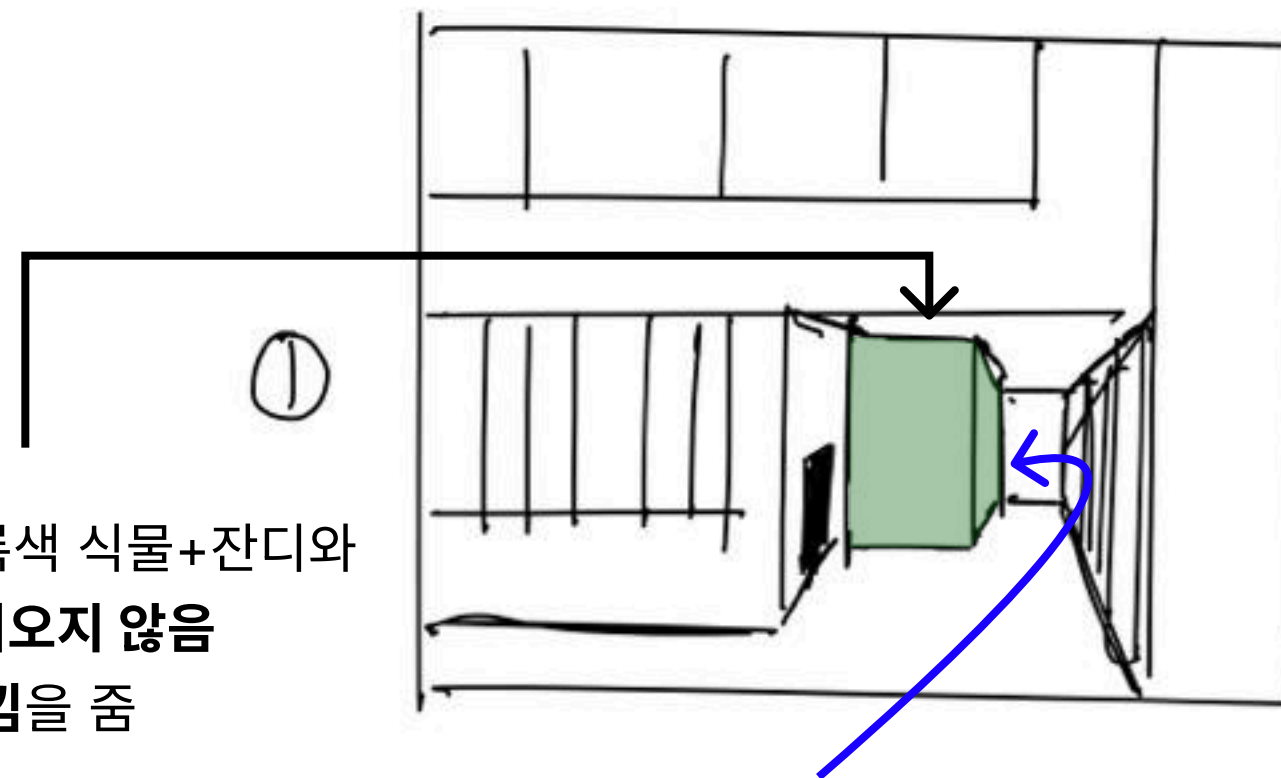


매스가 어두운 풀 색이라, 주위의 초록색 식물+잔디와 어우러져 멀리서 볼 때 시야에 잘 들어오지 않음
⇒ 위의 하얀 매스가 떠 있는 듯한 느낌을 줌

보가 없는 기둥이 이어지다가
입구쪽에는 역보 구조의 기둥이 등장

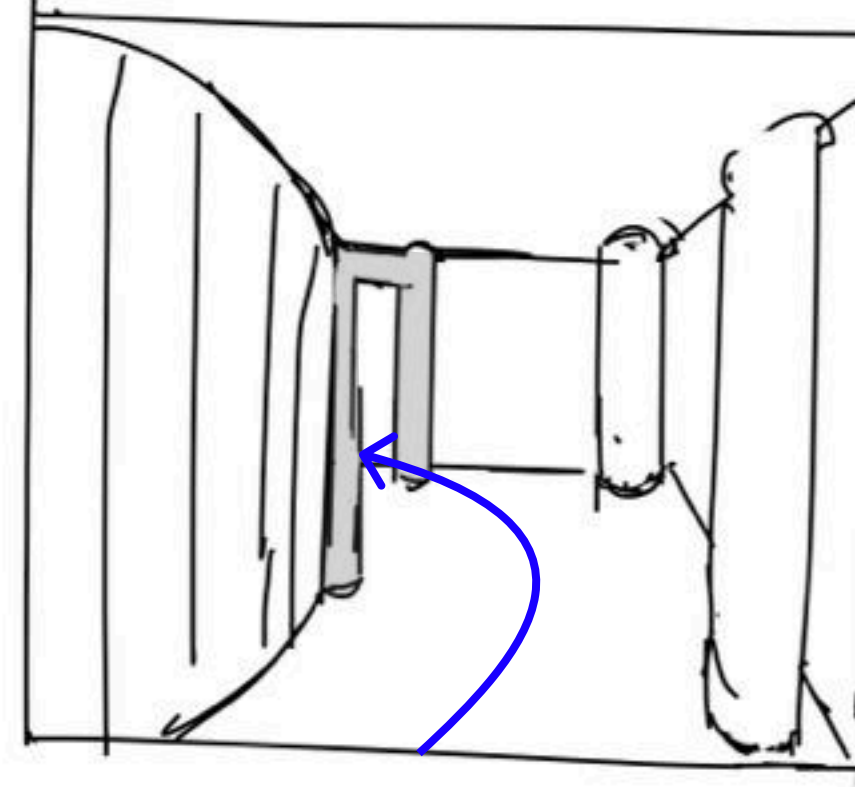


입구에서는 아예 보가 벽 안쪽으로 뚫고 들어가며
입구를 향한 방향성을 제시

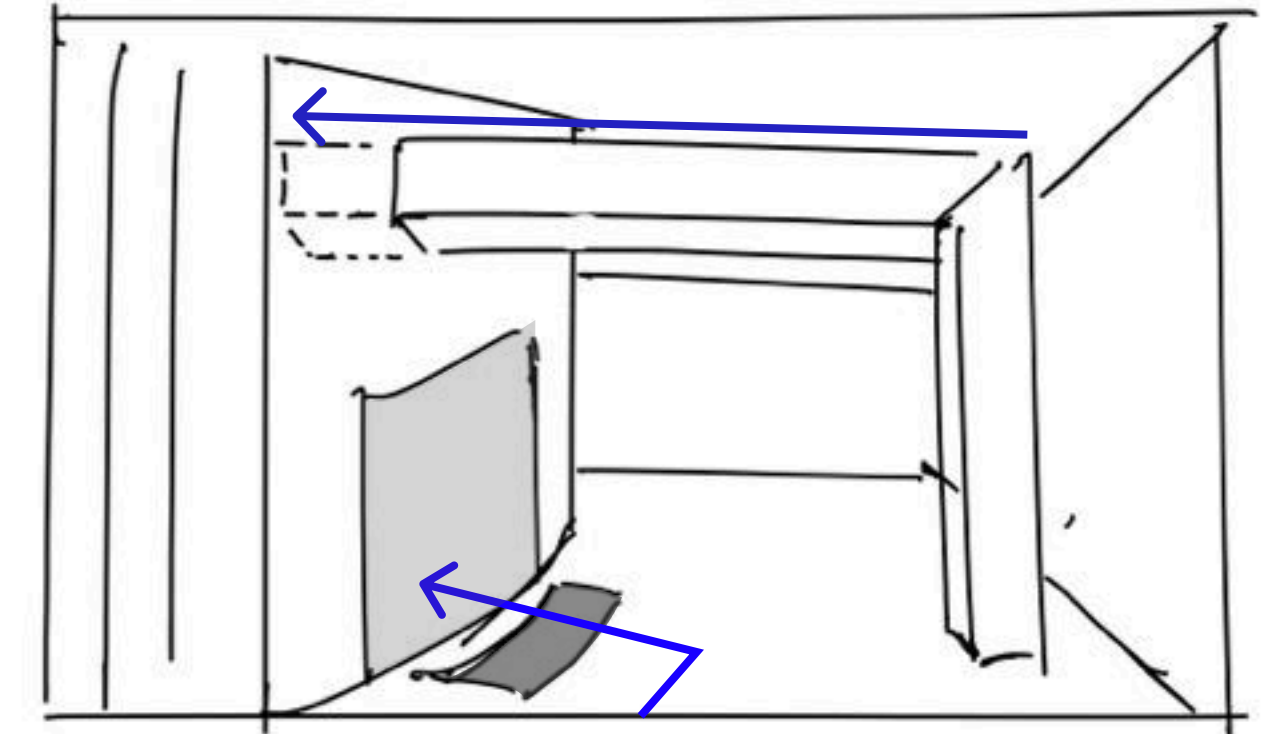


어두운 색의 현관발판이 입구로 유도

빌라 사보아 내부

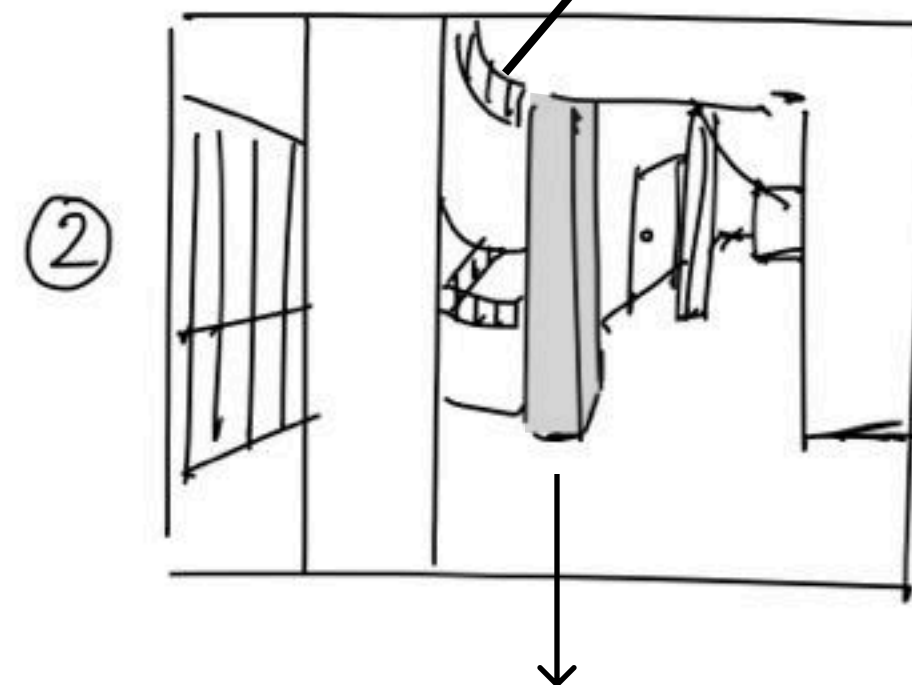

난간 없이 콘크리트를 높여 계단을 만들면 시야가 막히기 때문에 검은색의 난간 사용

내부의 기둥들이 다 둥근데, 이 기둥만 사각 기둥.
이 방향으로 진입하지 않도록 사람들을 밀어내는 역할

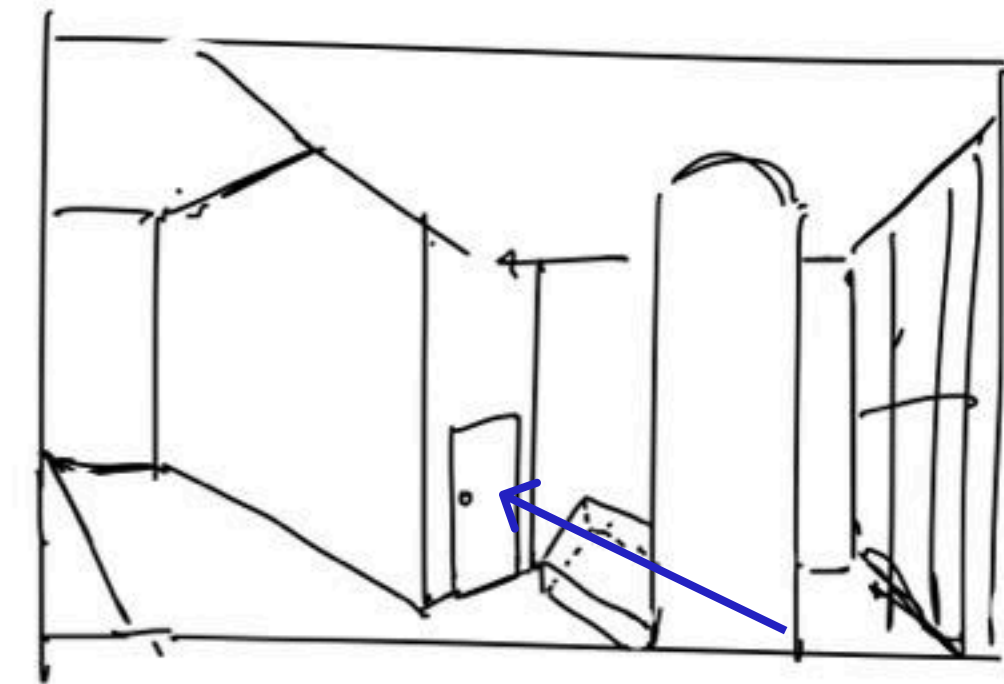

기둥에 테이블이 붙어있음
테이블의 방향이 사람들을 유도

기둥이 5개(3개+)가 나란히 있으면: **면처럼 인식됨**




가로로 긴 수평창

보가 있는 기둥이 3개 반복되어 리듬감을 형성

⇒ 3-4개 사이로 반복해야 적당한 리듬감, 그 이상으로 가면 남용

2개의 기둥 사이를 지나갈 때는: 문 사이를 지나는 것처럼 인식됨


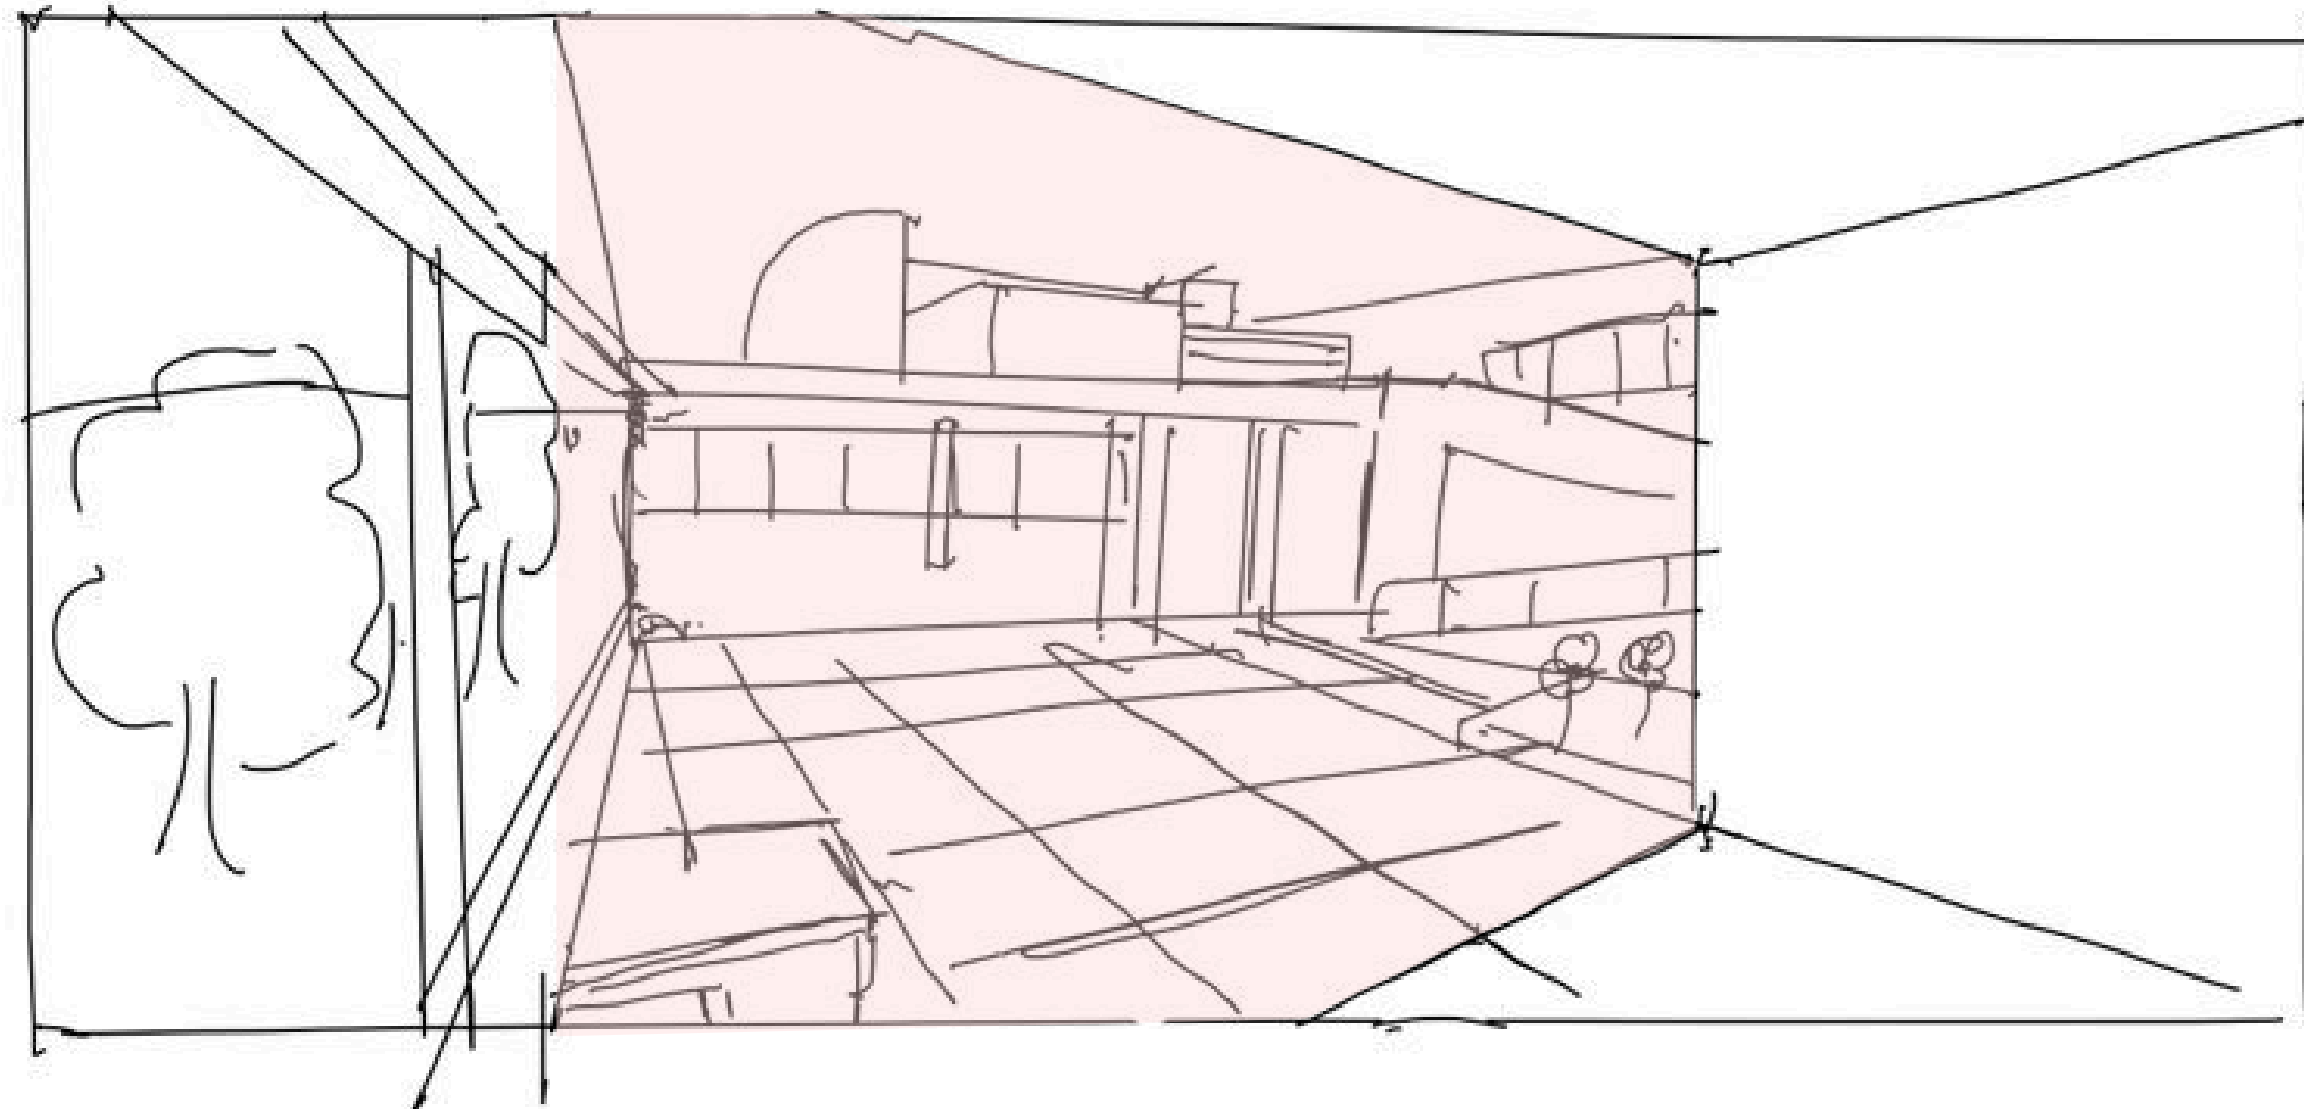


실내와 발코니 사이가 **프레임으로 구분**되듯이 설계
발코니는 **외부인 듯 내부인 듯** 오묘한 공간감을 갖게 됨

빌라 라 로셰

1. 입구 시야각 설계

AA'를 이은 직선은 입구에서 바로 보이는 시야각이지만,
BB'를 이은 직선은 입구에서 바로 보이지 않는 시야각이기 때문에,
사람들의 동선은 자연스럽게 **계단A로 유도된다.**

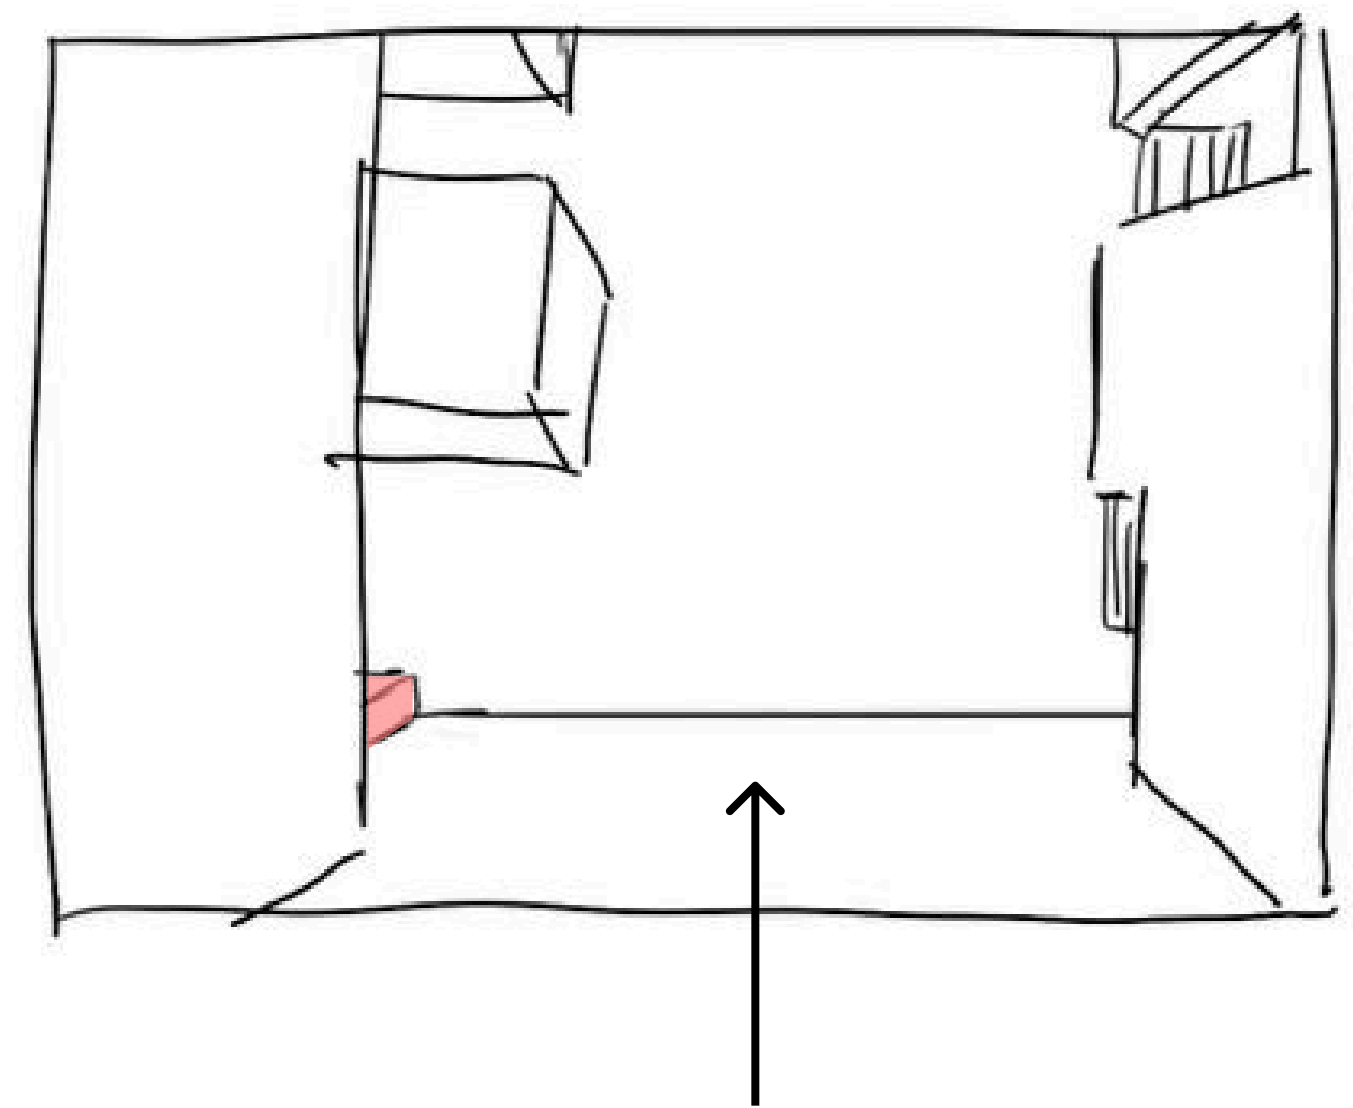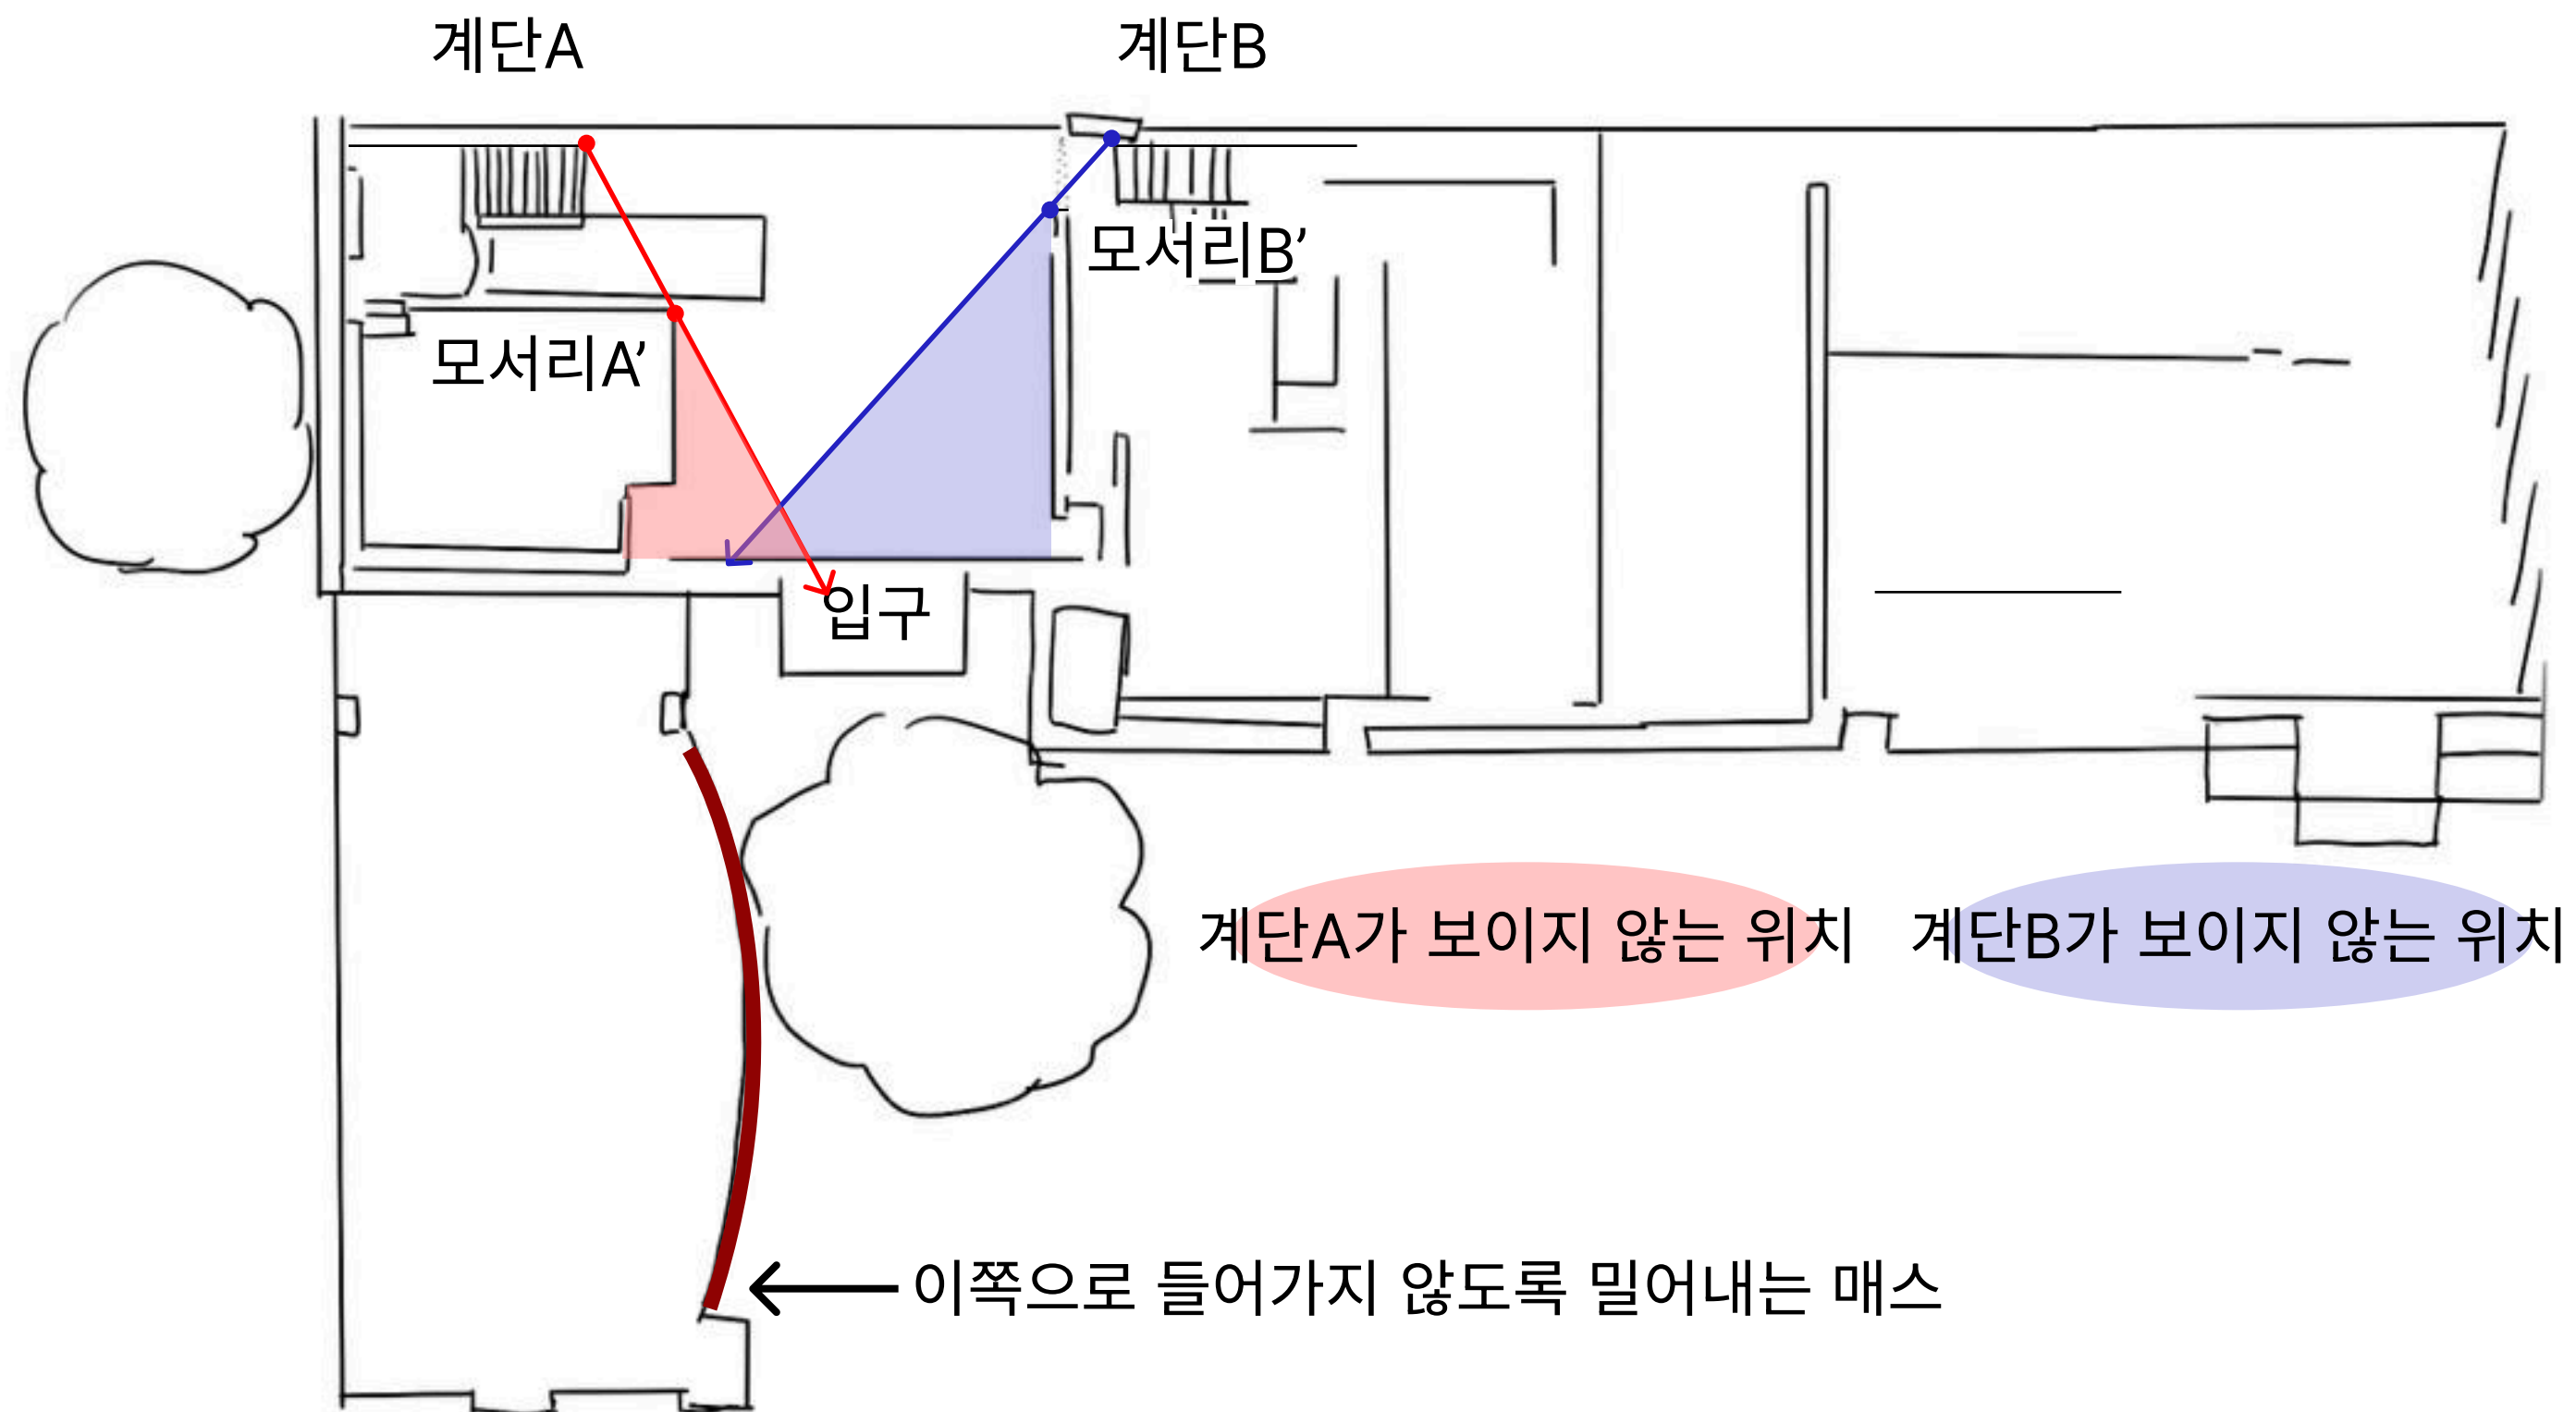


왼쪽 계단A가 오른쪽 계단B보다 먼저 시야에 들어와,
사람들은 **왼쪽으로 이동하도록 유도됨**

빌라 라 로세


2. 인간의 본능을 고려한 설계

외부

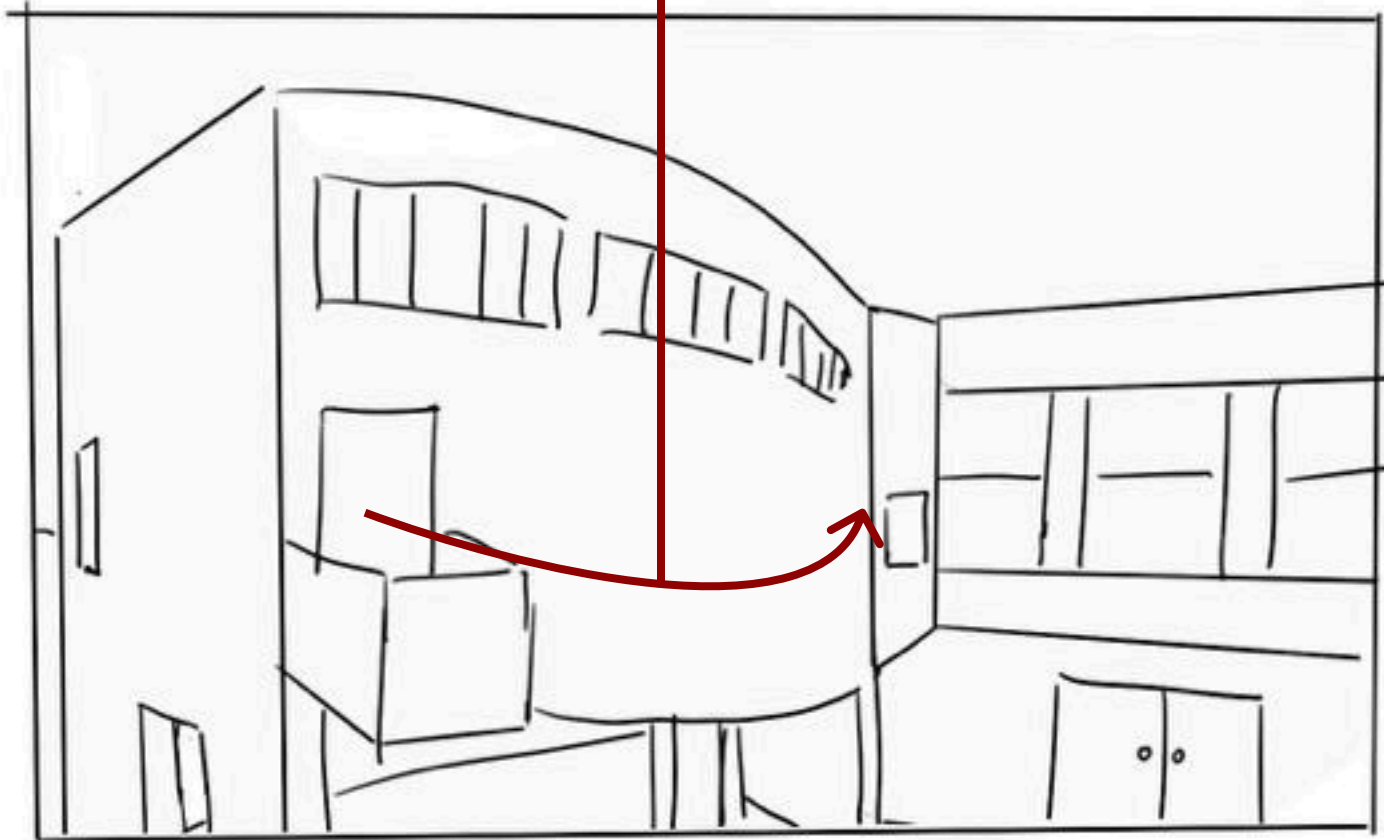


곡선 벽이 사람들을 밀어냄과 동시에
우측 건물로 진입할 것을 유도

내부

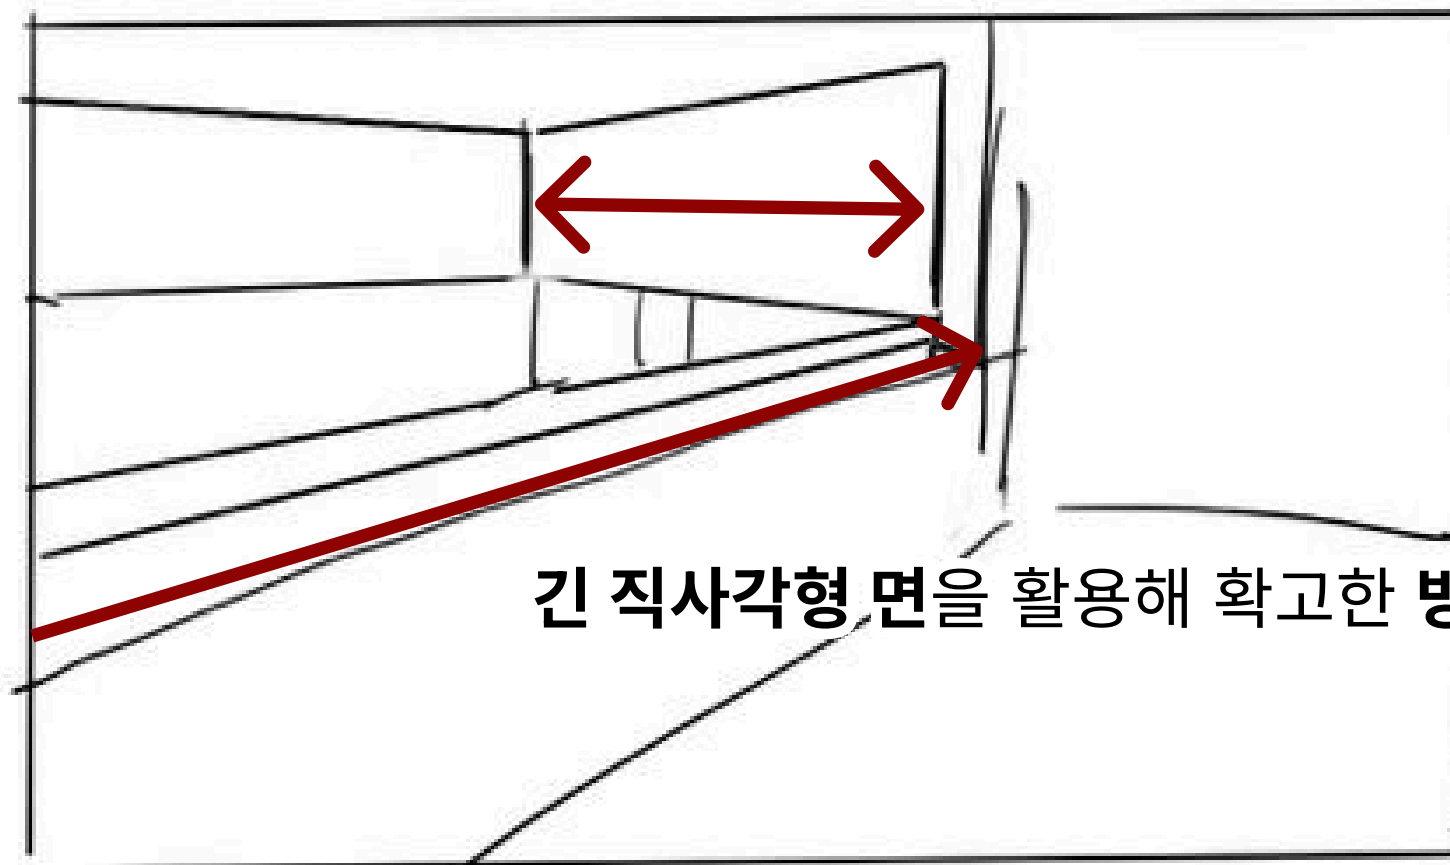

긴 직사각형 면을 활용해 확고한 방향성을 만들어냄

창문 사이의 간격이 점점 가까워져 방향감을 부여

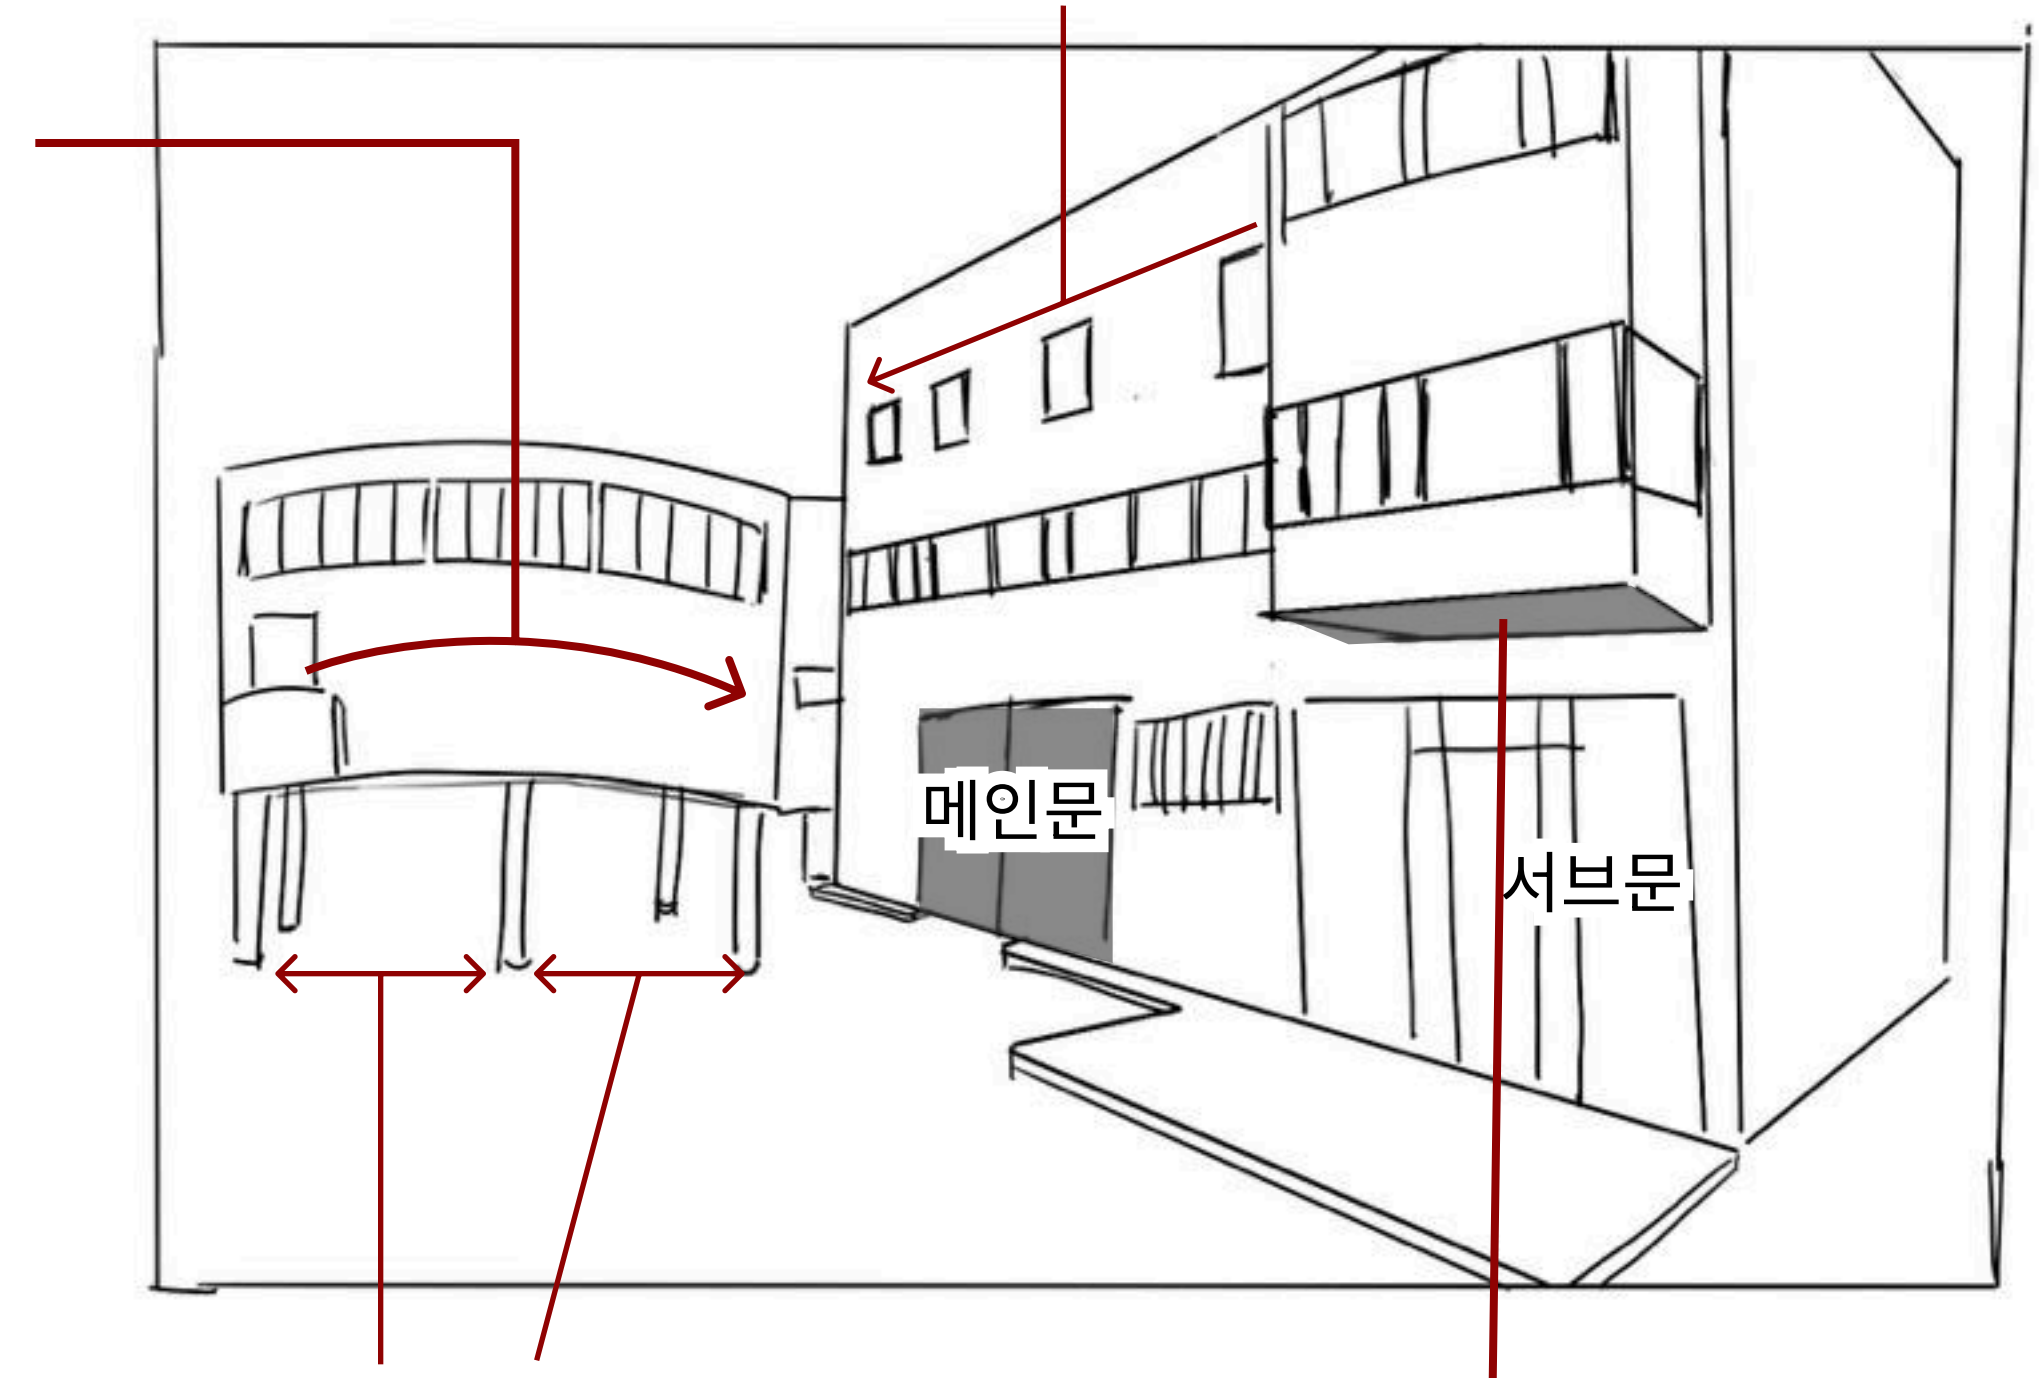


메인문

서브문

세 개의 기둥이 같은 거리를 두고 배치되어
기둥과 기둥 사이가 문처럼 느껴지지 않음
이 또한 이 건물로 사람들을 유도하지 않기 위함

인간은 수렵채집의 특성을 갖고 있기에, 본능적으로
비를 피하기 위한 처마에 시선이 가게 됨
입구 위에 처마를 만들어 진입을 유도

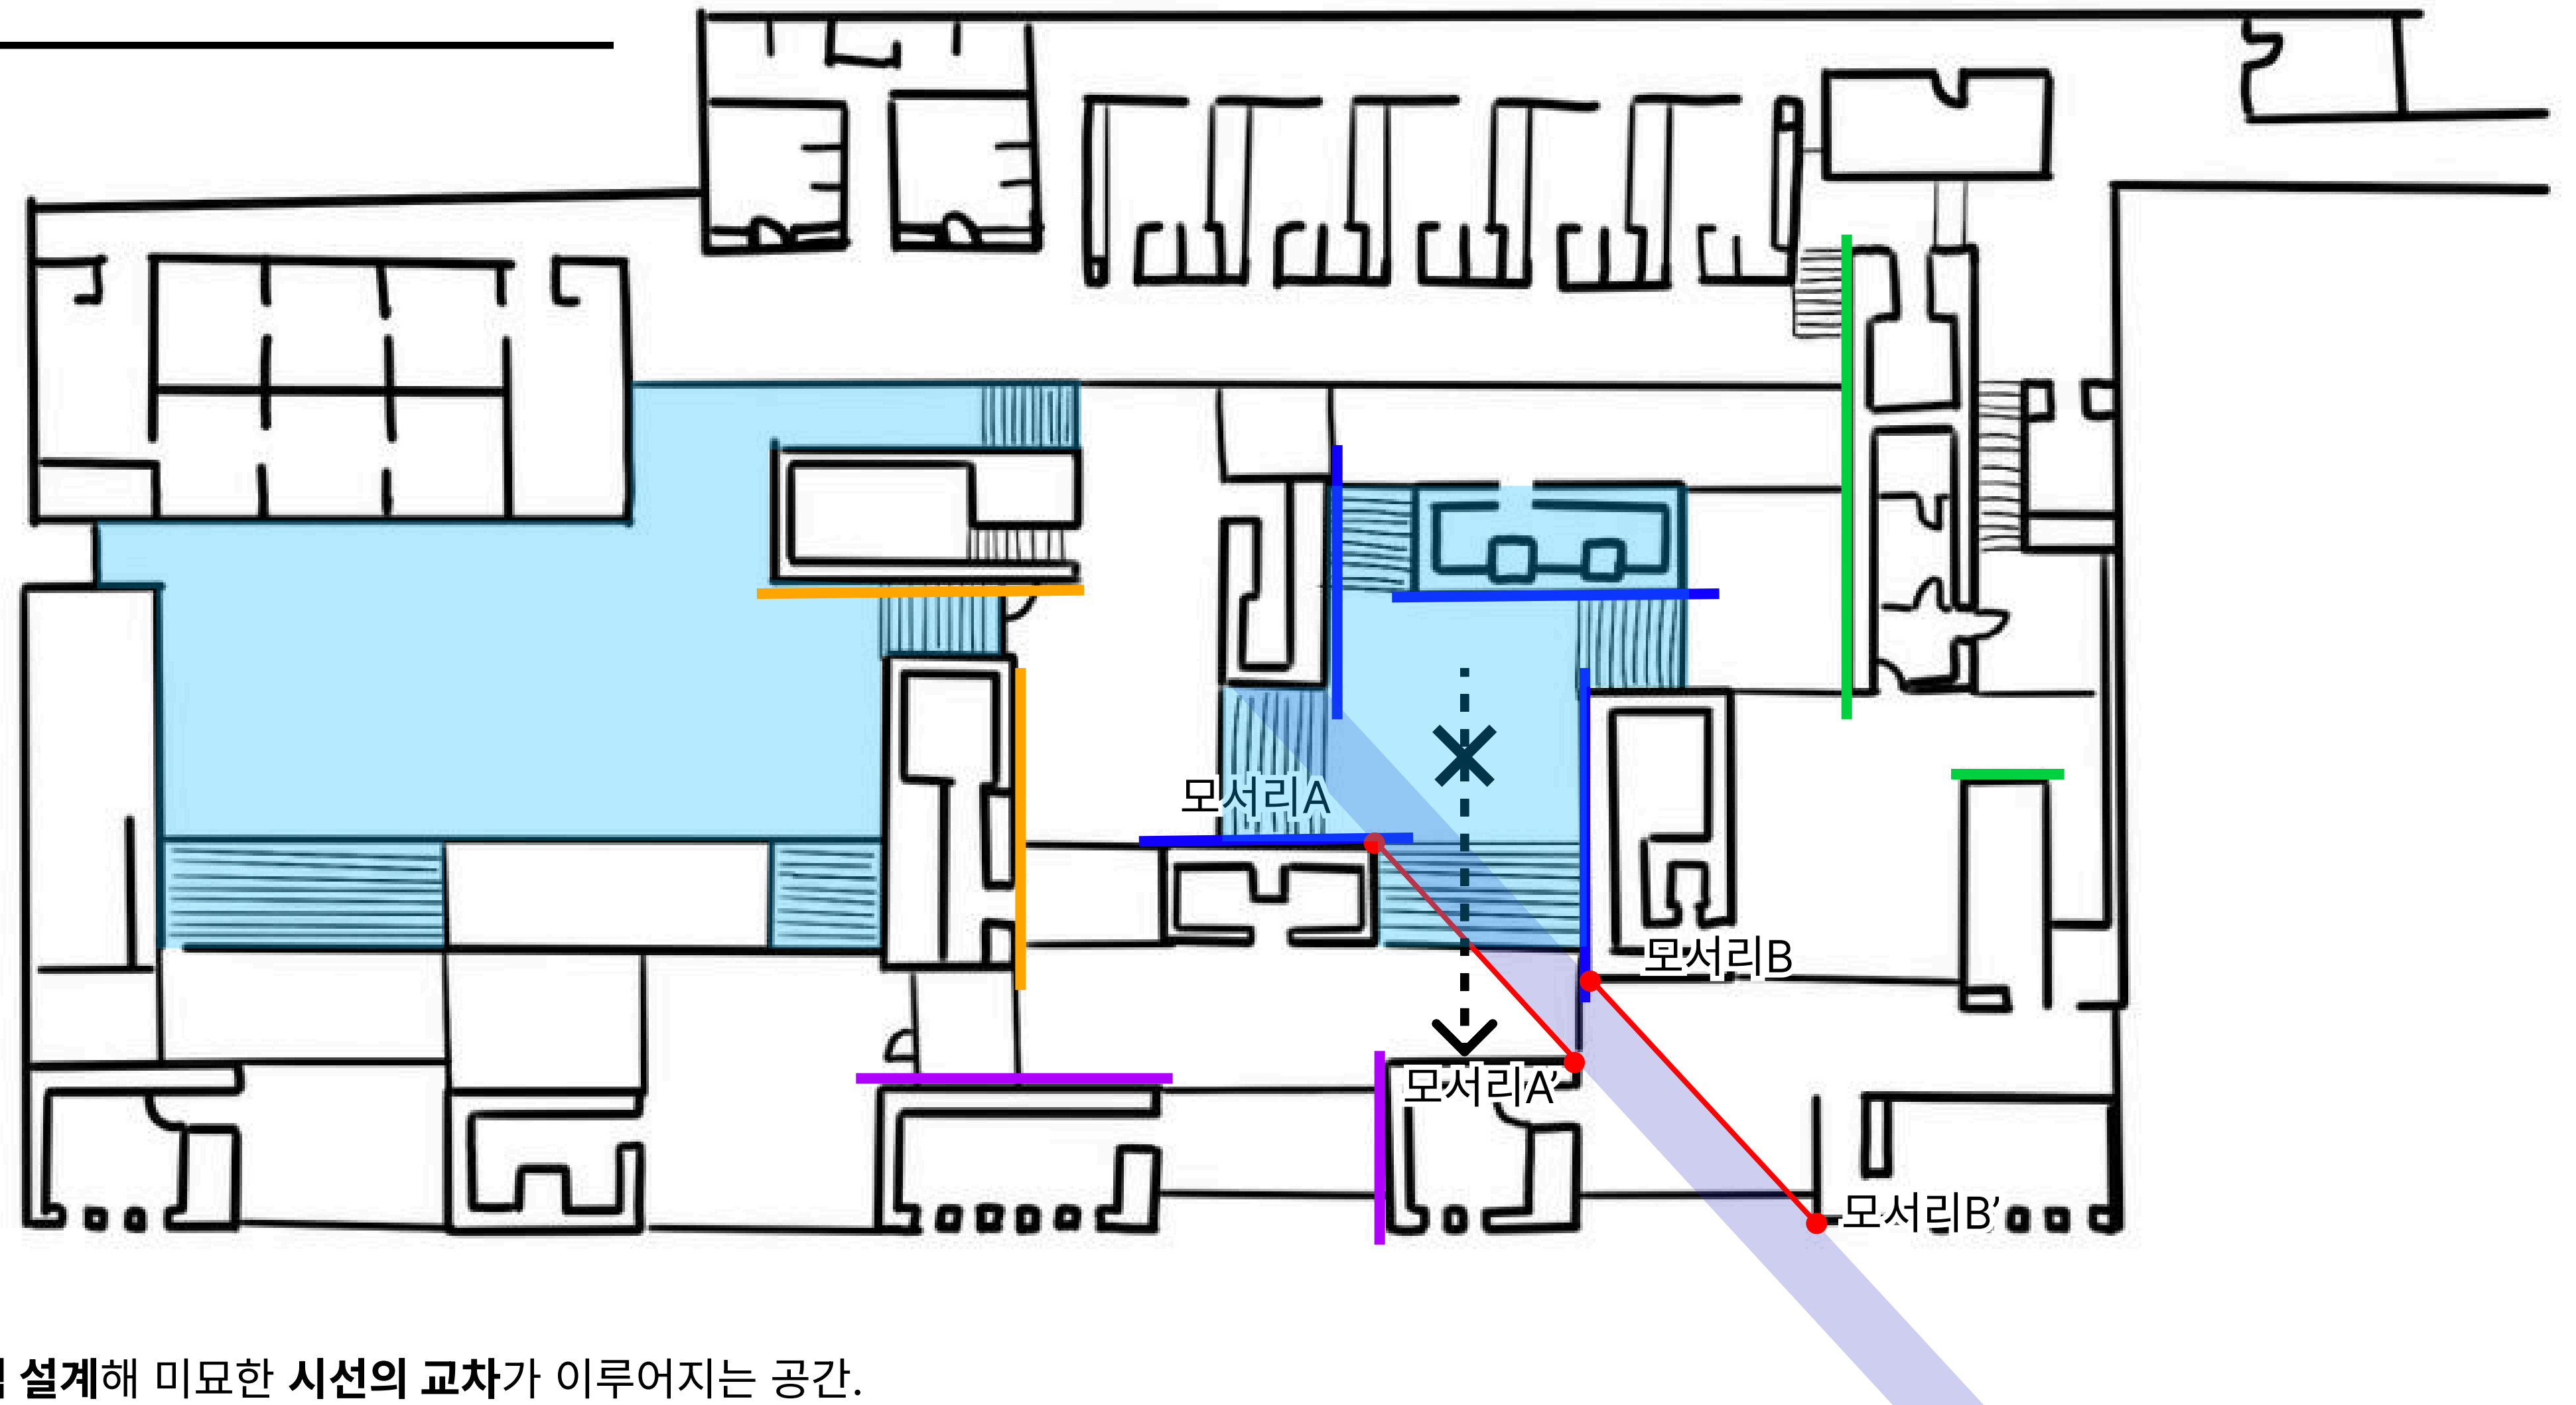


공간을 바람개비처럼 설계해 미묘한 시선의 교차가 이루어지는 공간.


예를 들어, 오른쪽의 온천에 들어갔을 때

벽과 벽 사이 살짝만 드러나는 선분 AA', BB' 사이의 공간으로 알프스의 풍경을 바라볼 수 있게 설계되어 있다.

들쭉날쭉한 벽이 리듬감을 형성하는 것이 특징.

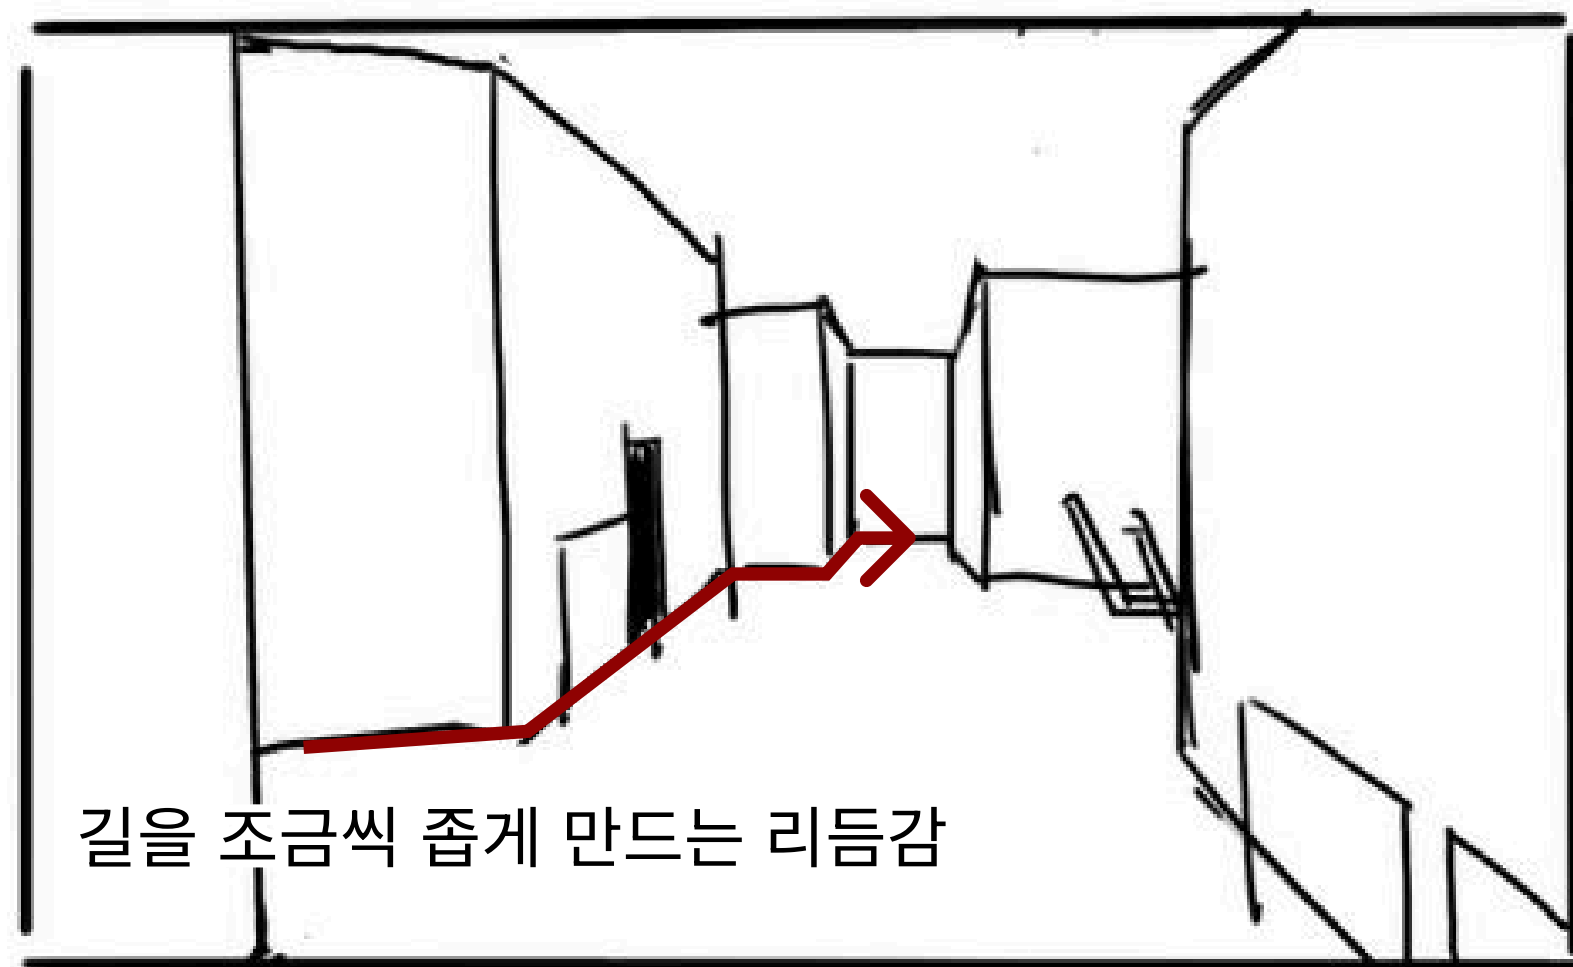

입구에서 탈의실로 들어갈 때,
좁은 틈 사이로 내부공간을 살짝 보여줘 예습할 수 있도록 만든다.

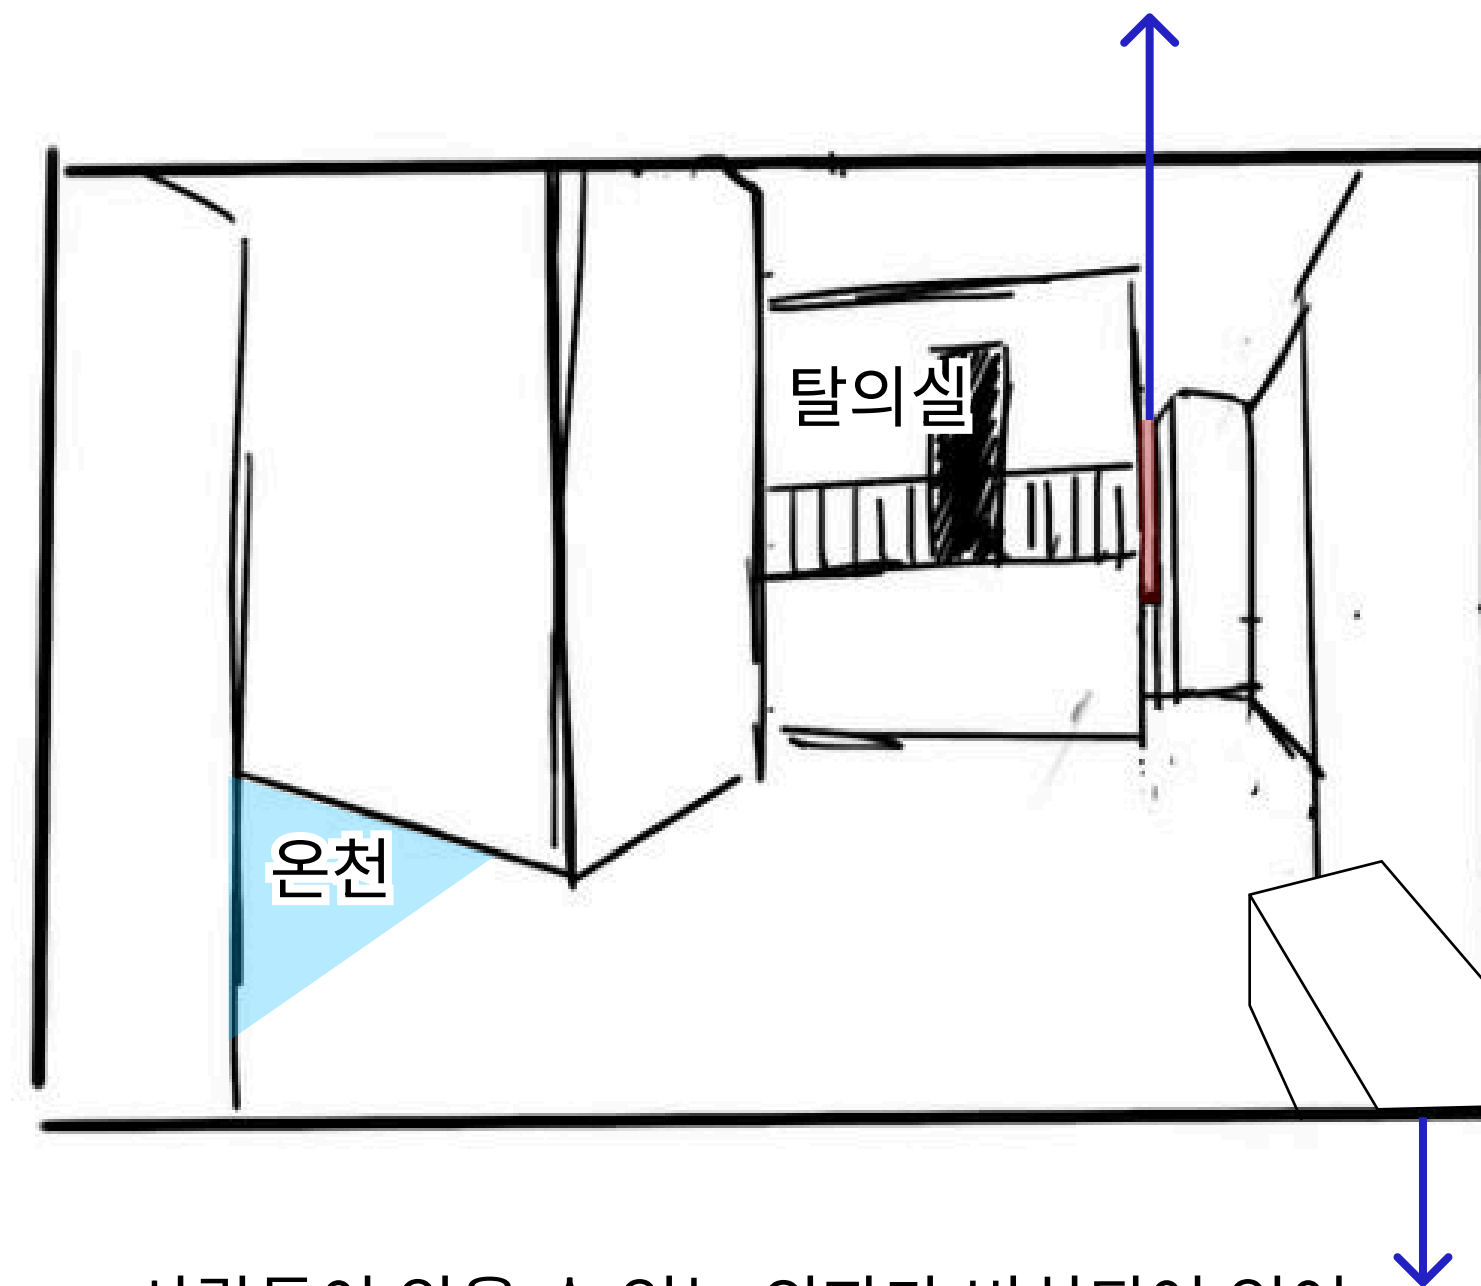

사람들이 앉을 수 있는 의자가 비치되어 있어,
이미 온천에 들어온 사람들은 입구를 지나가는 사람들을 보고
저 공간이 자신들이 이미 지나온 입구 공간이었다는 사실을 환기(복습)한다.